




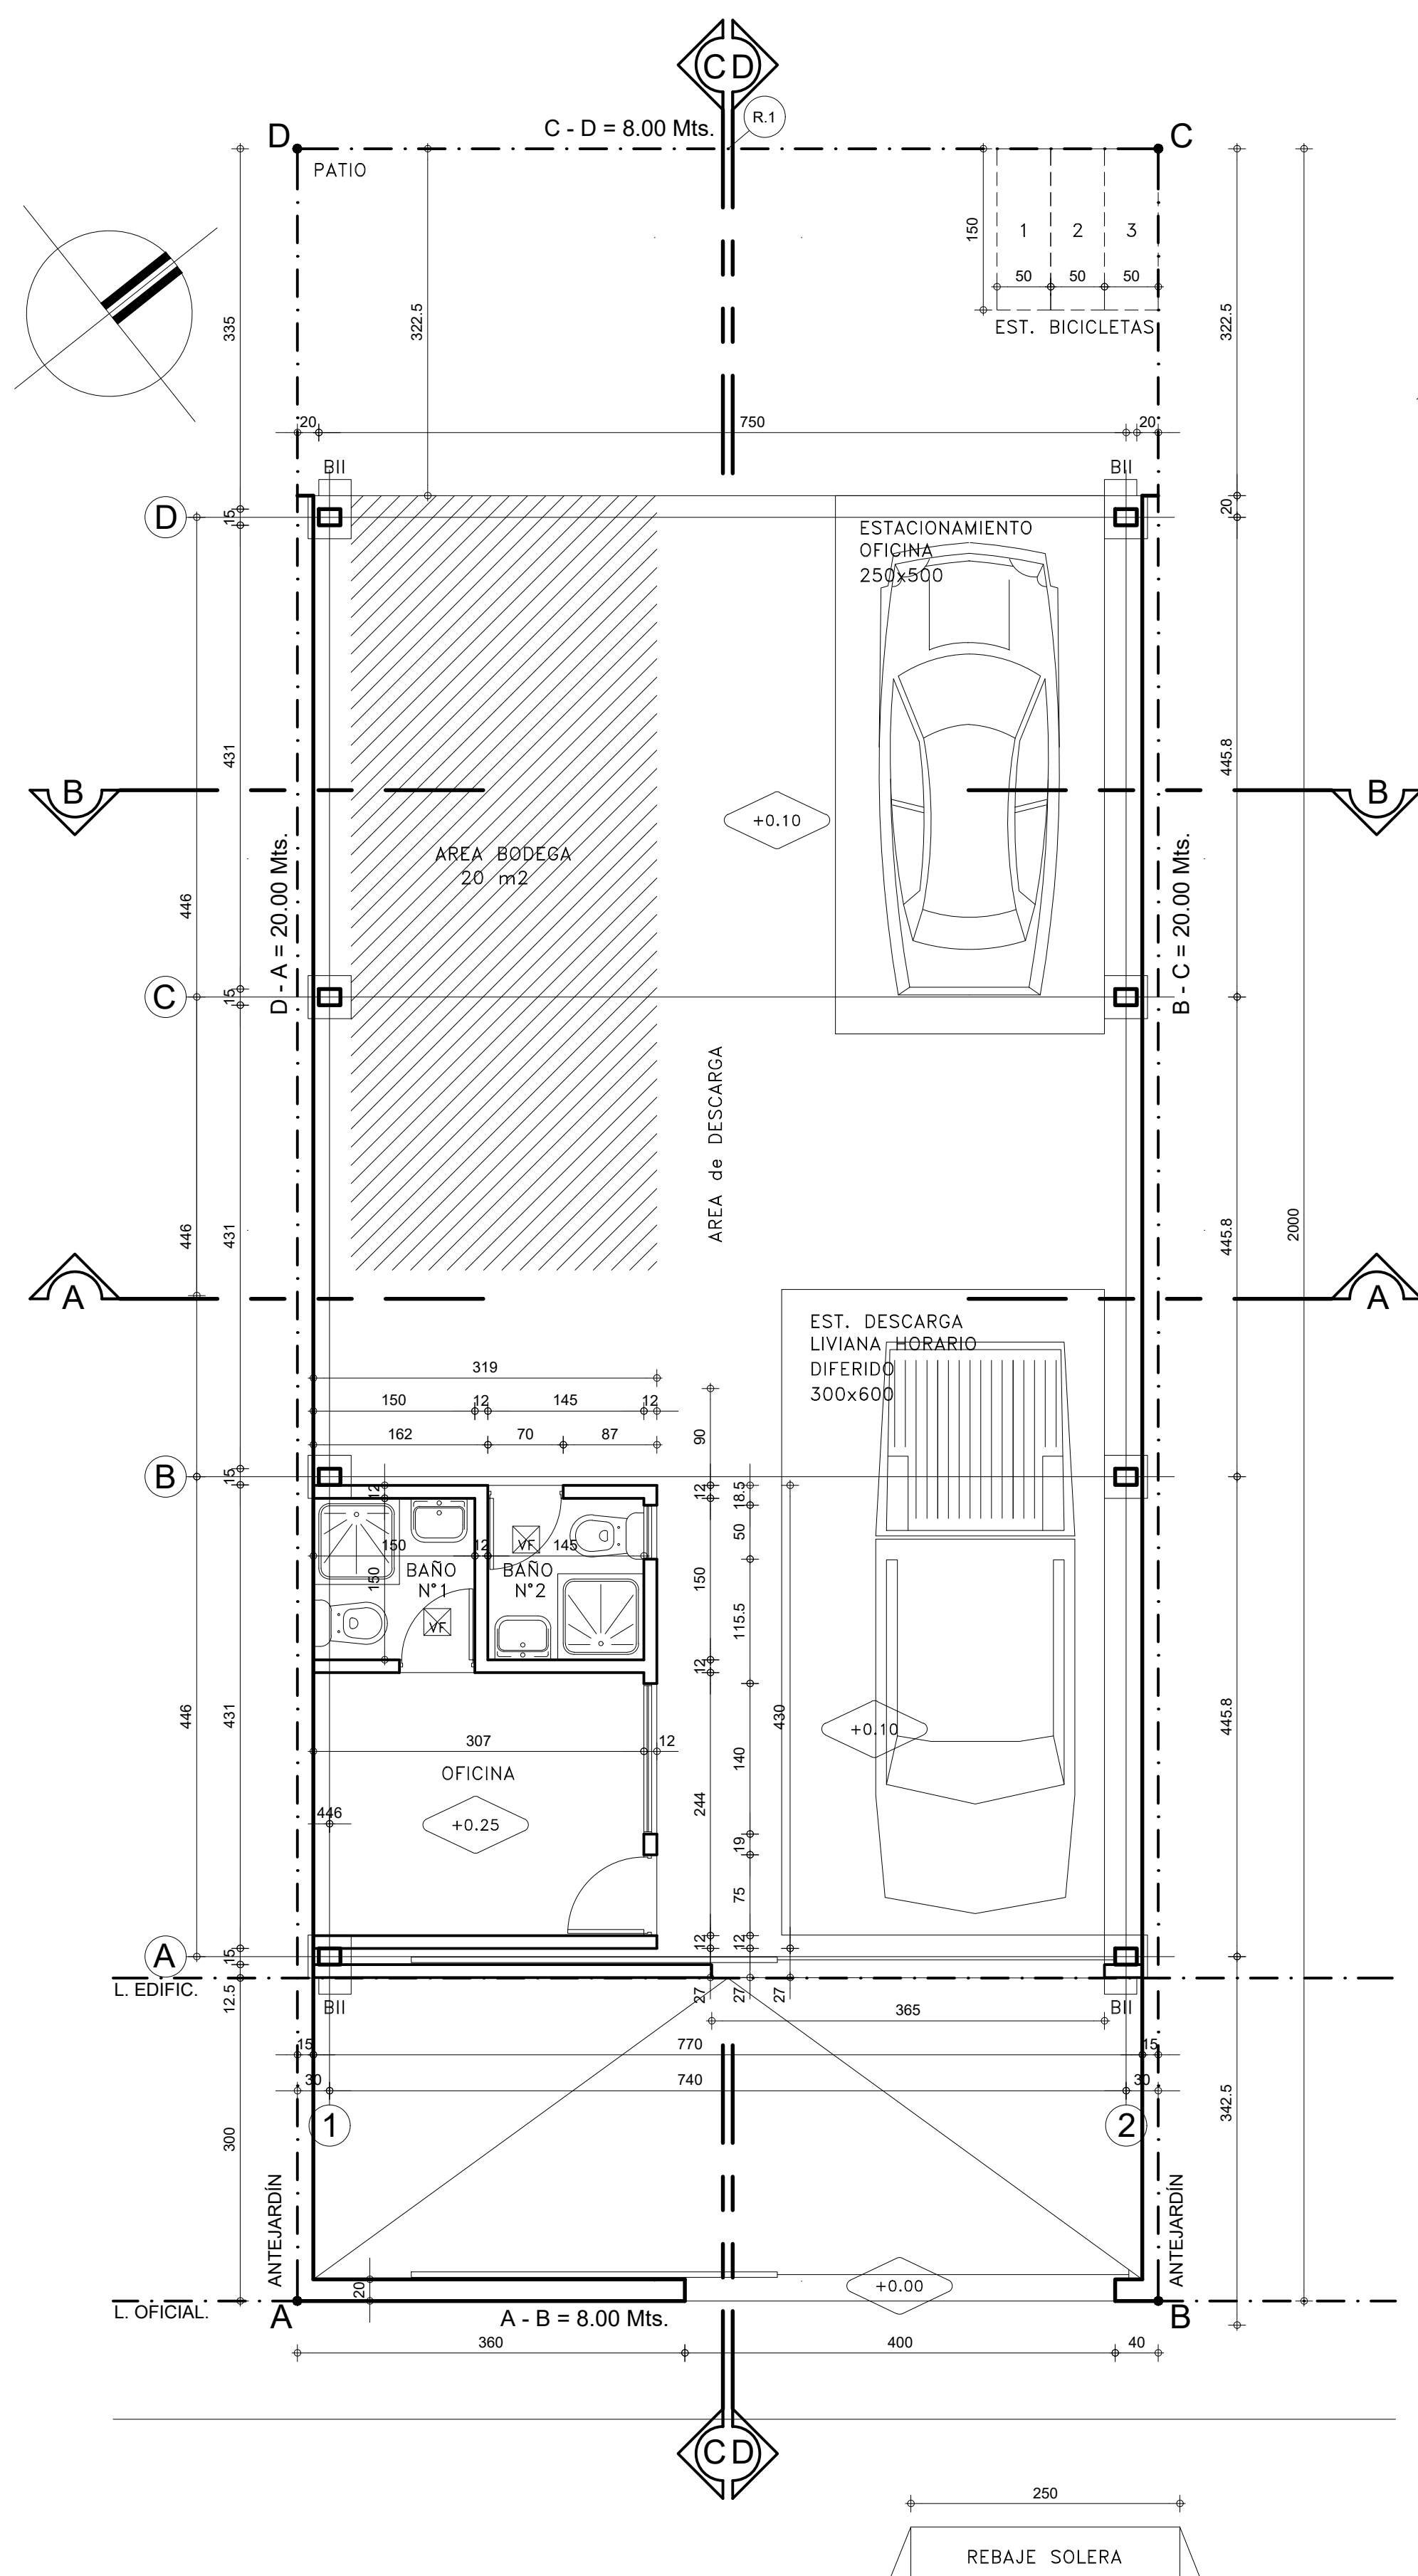

1 PLANTA ARQUITECTURA
1:50

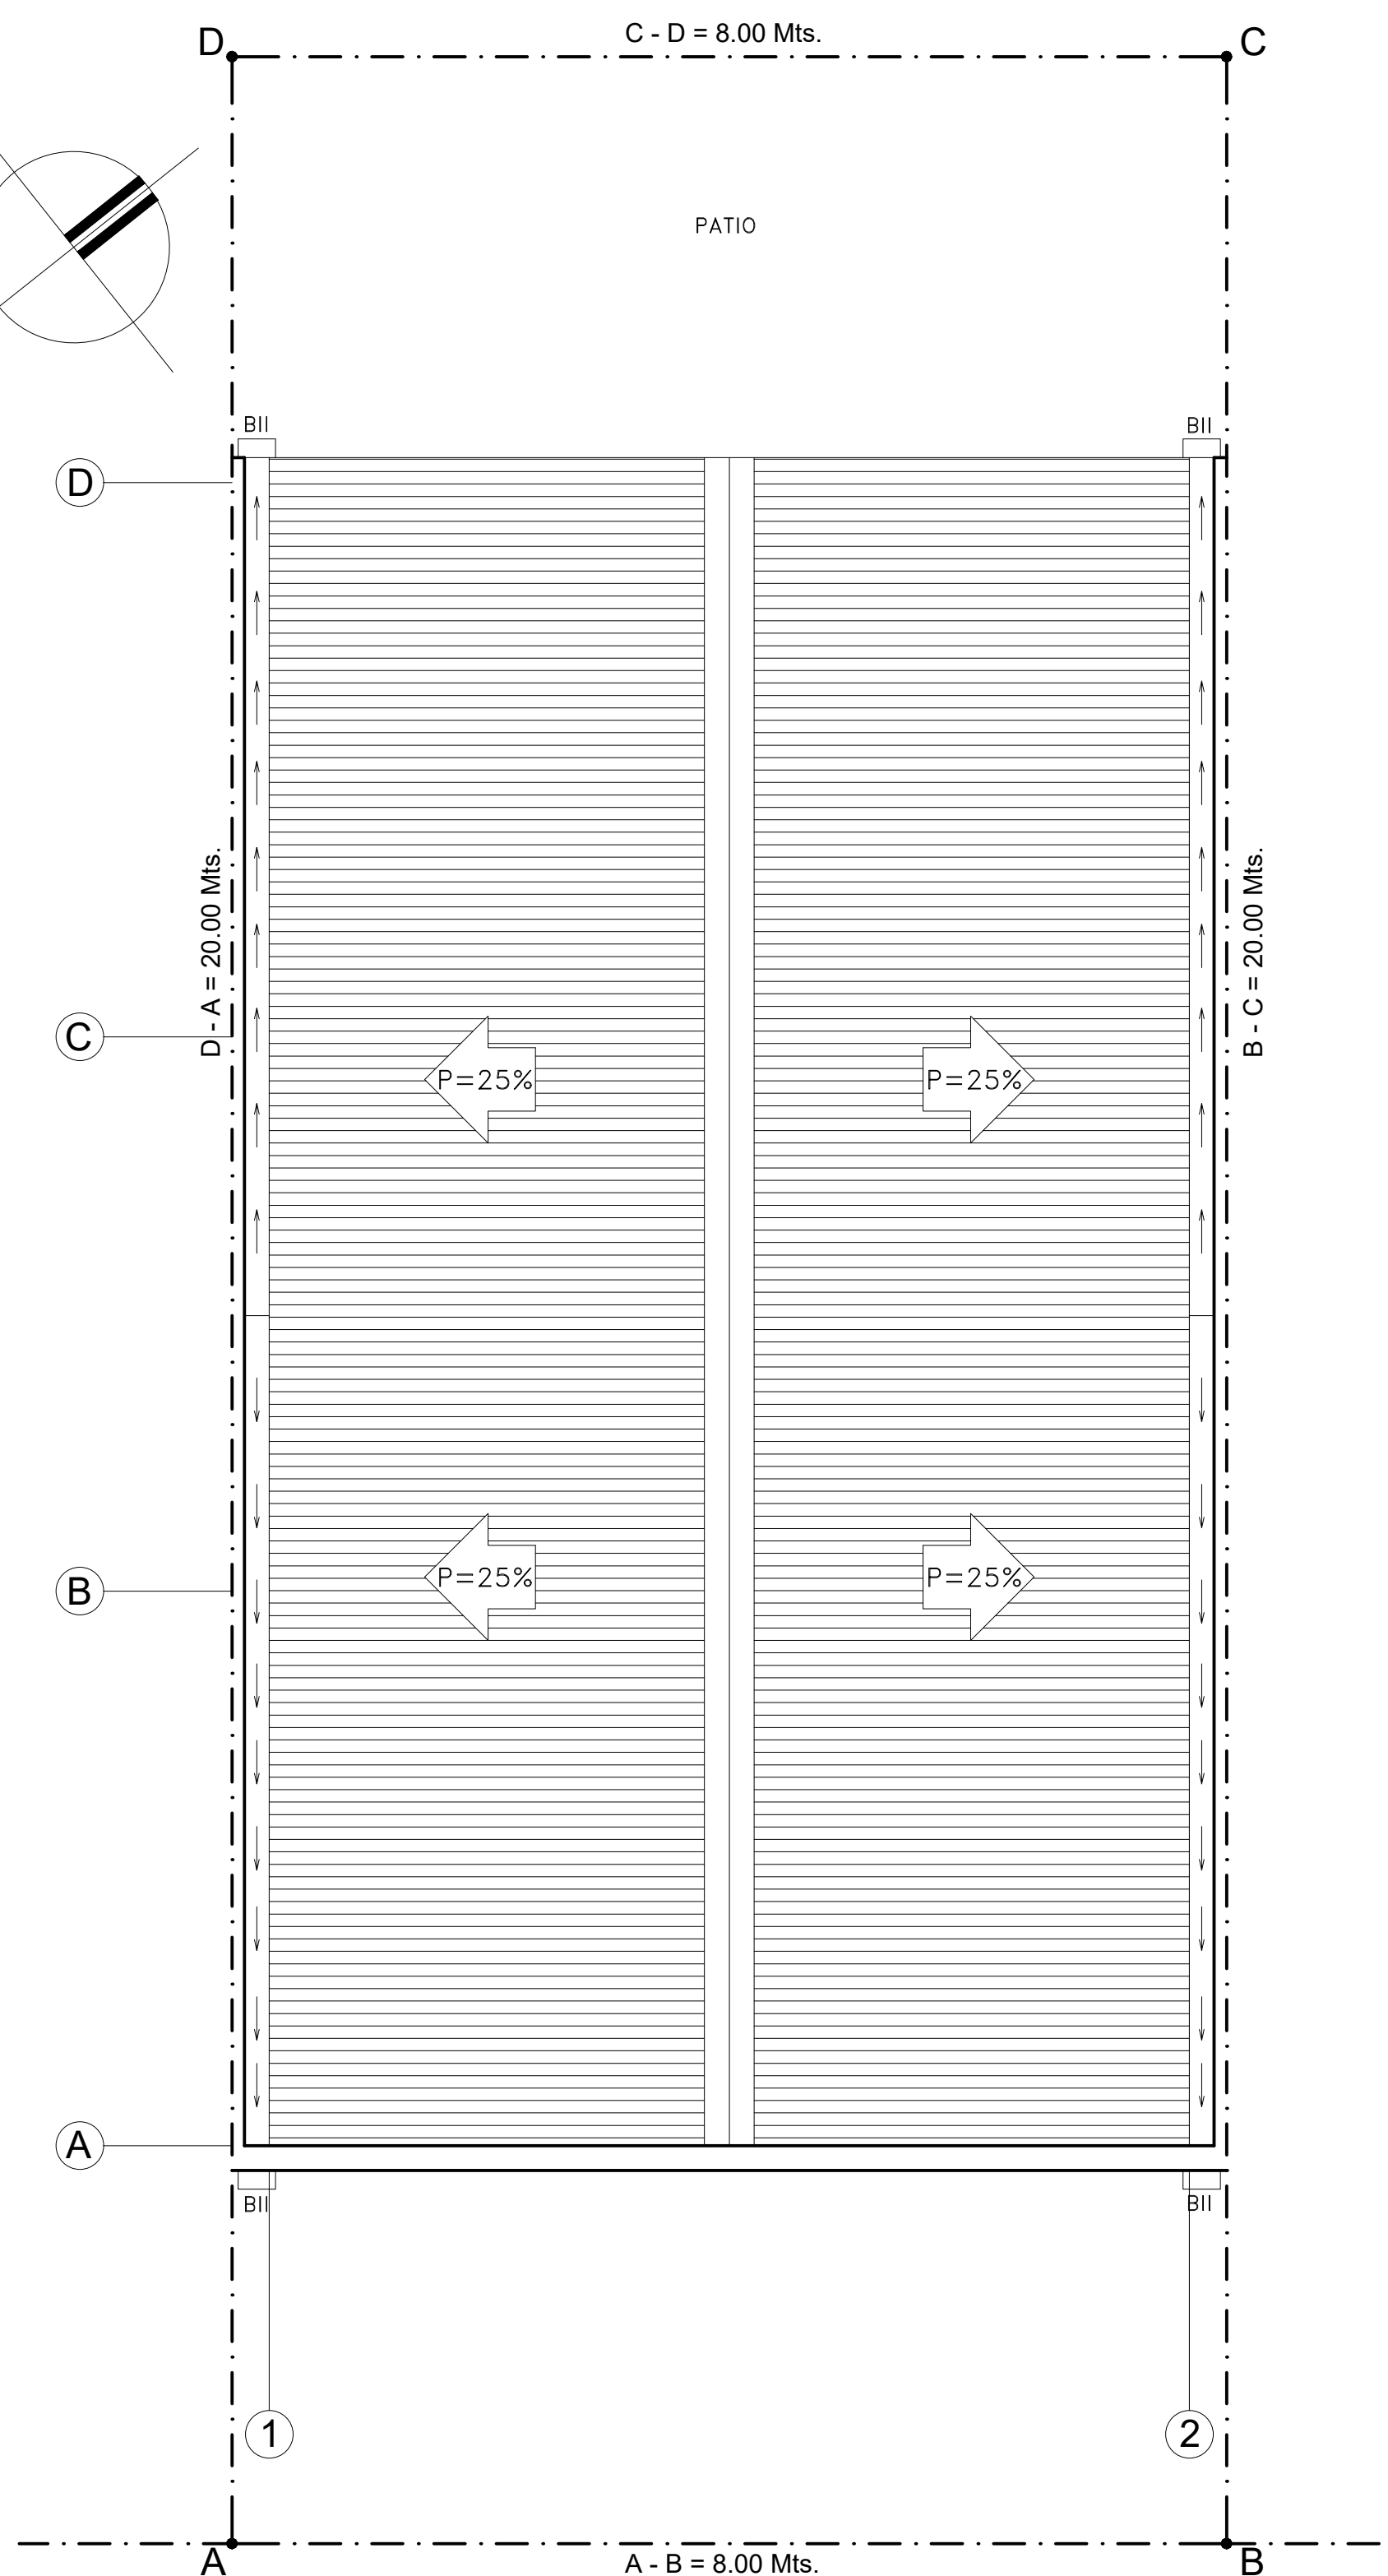


2 PLANTA DE CUBIERTA
1:50

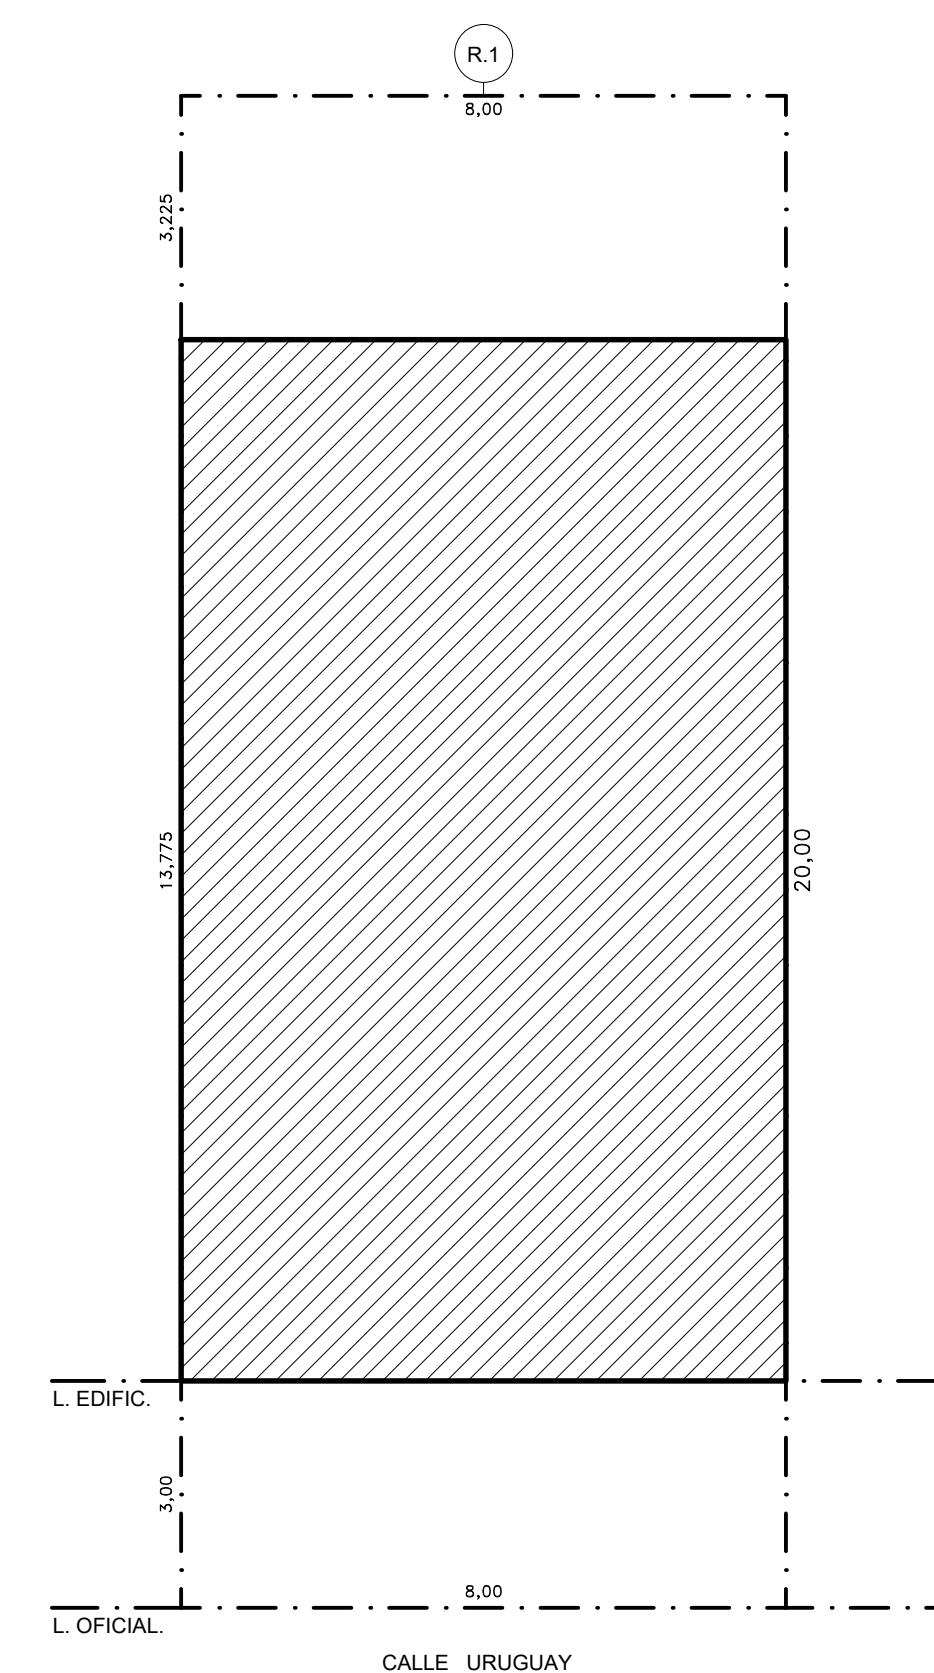


3 EMPLAZAMIENTO
1/100

CUADRO DE SUPERFICIE				
SUPERFICIE PROYECTADA EN 1° PISO				
N°	RECUADROS	CONSTRUIDO	FACTOR	IMPONIBLE
A	8.00 x 6.00	48.00	1	48.00
B	8.00 x 8.00/2	32.00	1	32.00
TOTAL SUPERFICIE		80.00 m2		
SUPERFICIE TERRENO		= 160,00	mts2=	100 %
OCUPACION SUELO		= 80,00	mts2=	50 %
CONSTRUCTIBILIDAD		= 80,00	mts2=	50 %
ESTACIONAMIENTOS				
APLICACIÓN SEGUN ART. 5.2.4.				
OFICINA 1c3 Of. =1; ALMACENAMIENTO COMP.TIPO2 =1				
REQUERIDO OFICINA = 1				
REQUERIDO ALMACENAMIENTO = 1 DE CARGA Y DESC.1				
PROPUESTO OFICINA = 1				
PROPUESTO ALMACENAMIENTO =1 CARG/DES (USO DIF.)				
EST. BICICLETAS REQUERIDO = 1, PROPUESTOS = 3				

5 SUPERFICIE
1:100

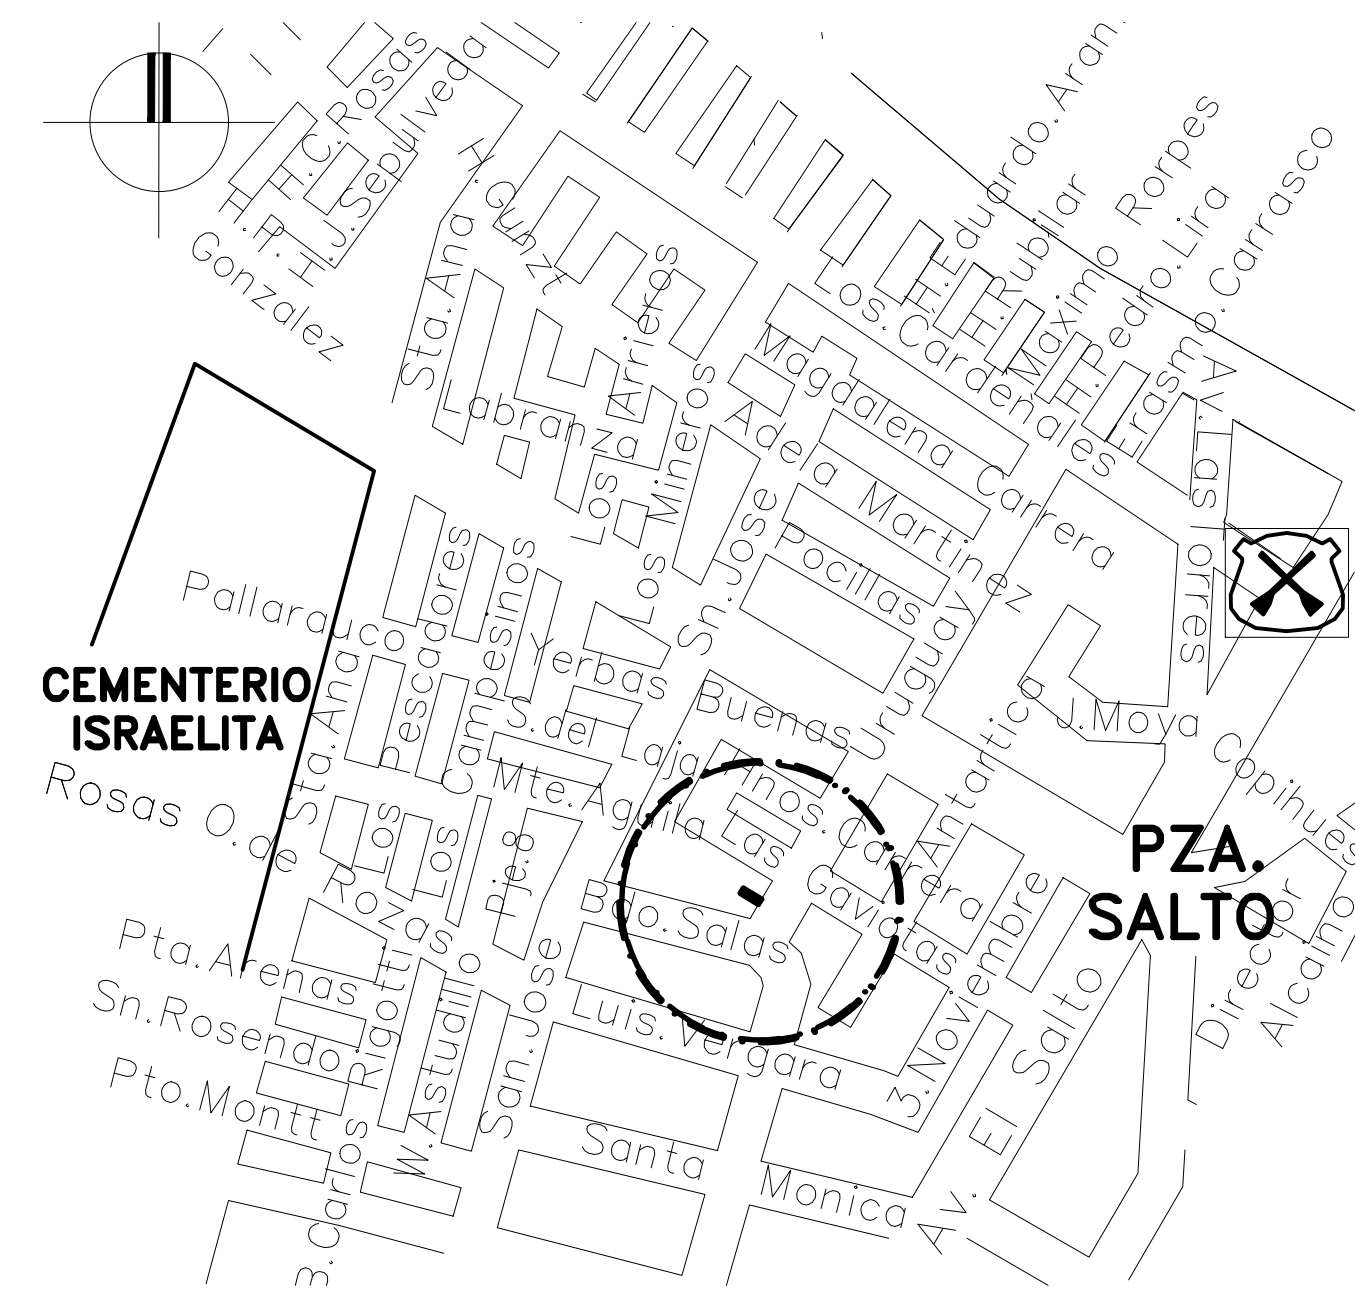

4 UBICACION
S/ESC

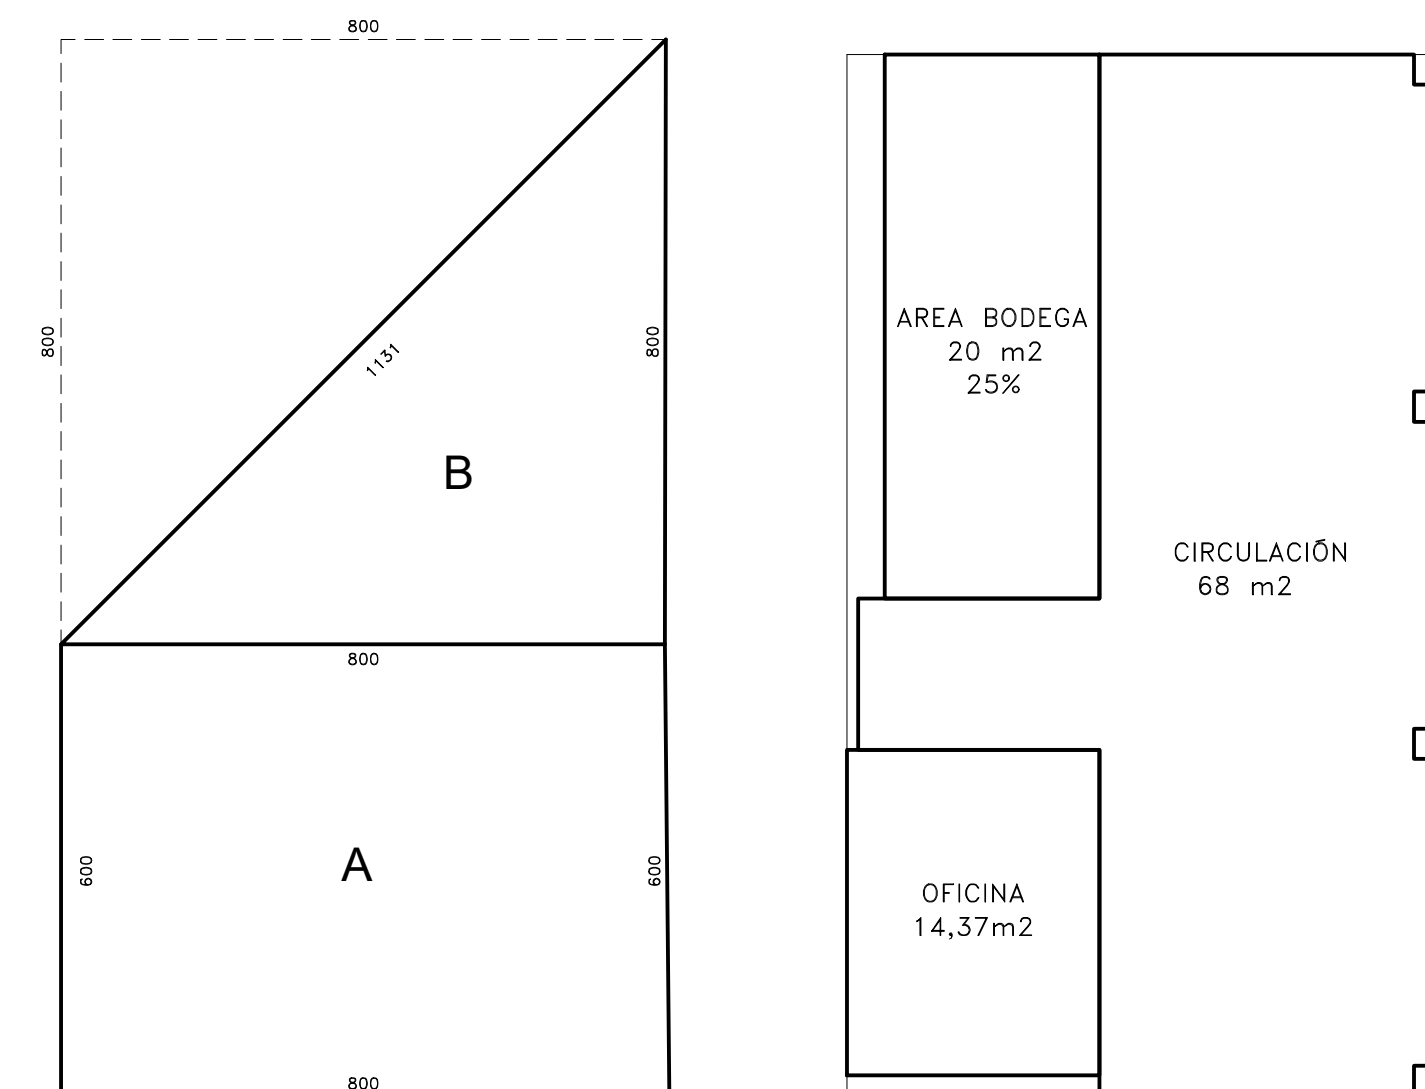

6 SUPERFICIE USOS
1:100

OBRA NUEVA BODEGA COMPLEMENTARIA TIPO 2				URUGUAY N°3134	
ILUSTRE MUNICIPALIDAD DE RECOLETA				COMUNA : RECOLETA	
MATERIA PLANTA DE ARQUITECTURA PLANTA DE CUBIERTA SUPERFICIE UBICACION				PROPIETARIO PABLO ERASMO RIVERA ONETTO C/I 8.826.691-9	
DIBUJO JOSE SAEZ I.				ARQUITECTO GUSTAVO RIOSERO MARTINEZ C.I. 10.390.900-7	
REVISOR G.R.M.				ROL 6070-15	
ESCALA INDICADAS				FECHA 11-06-20	
LAMINA 1 de 3					