
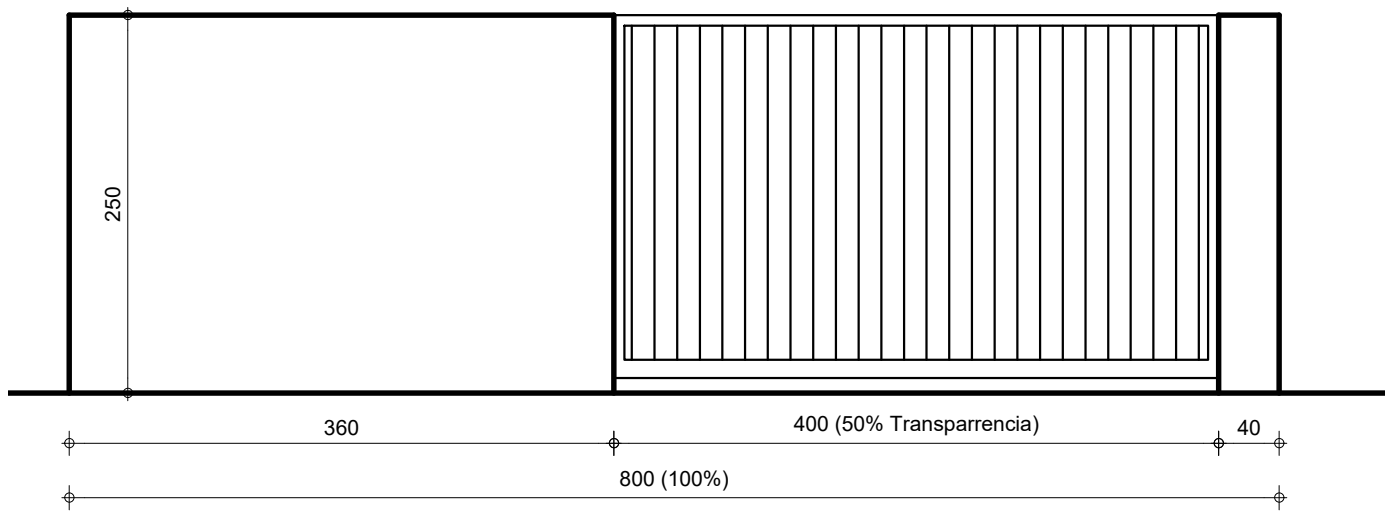
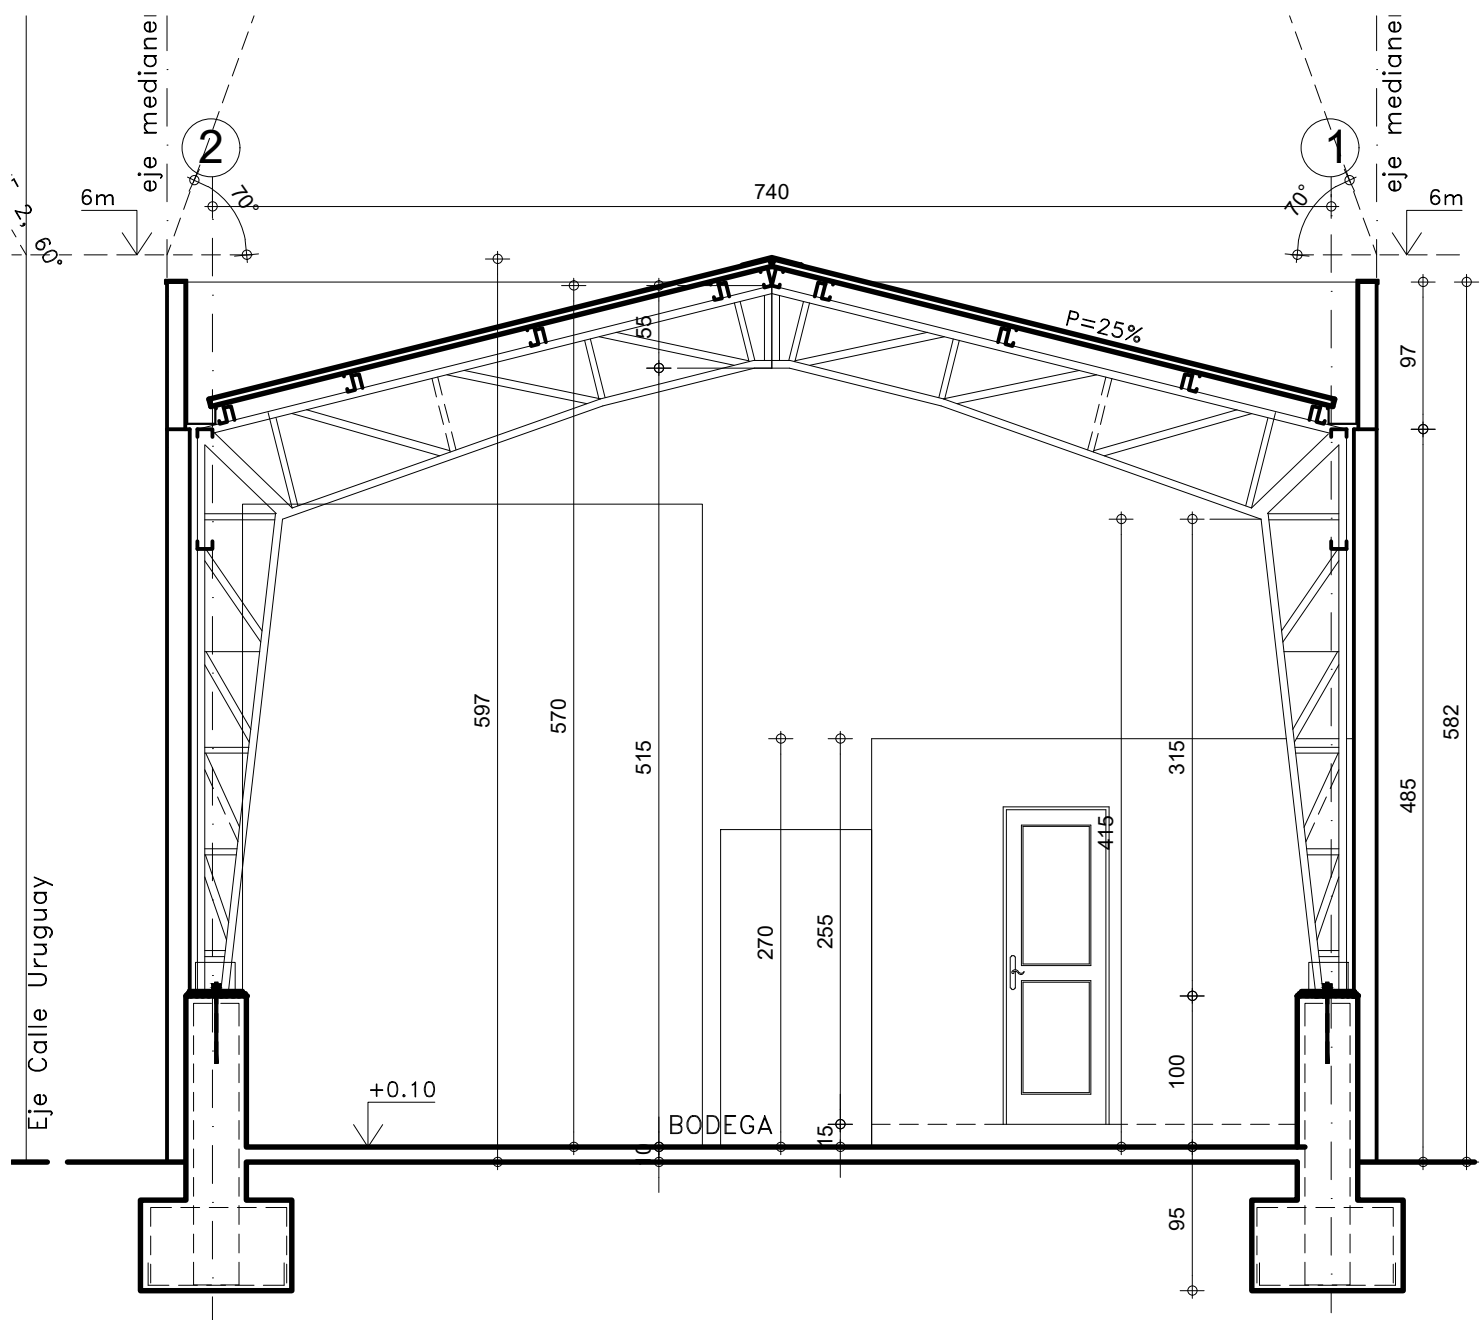
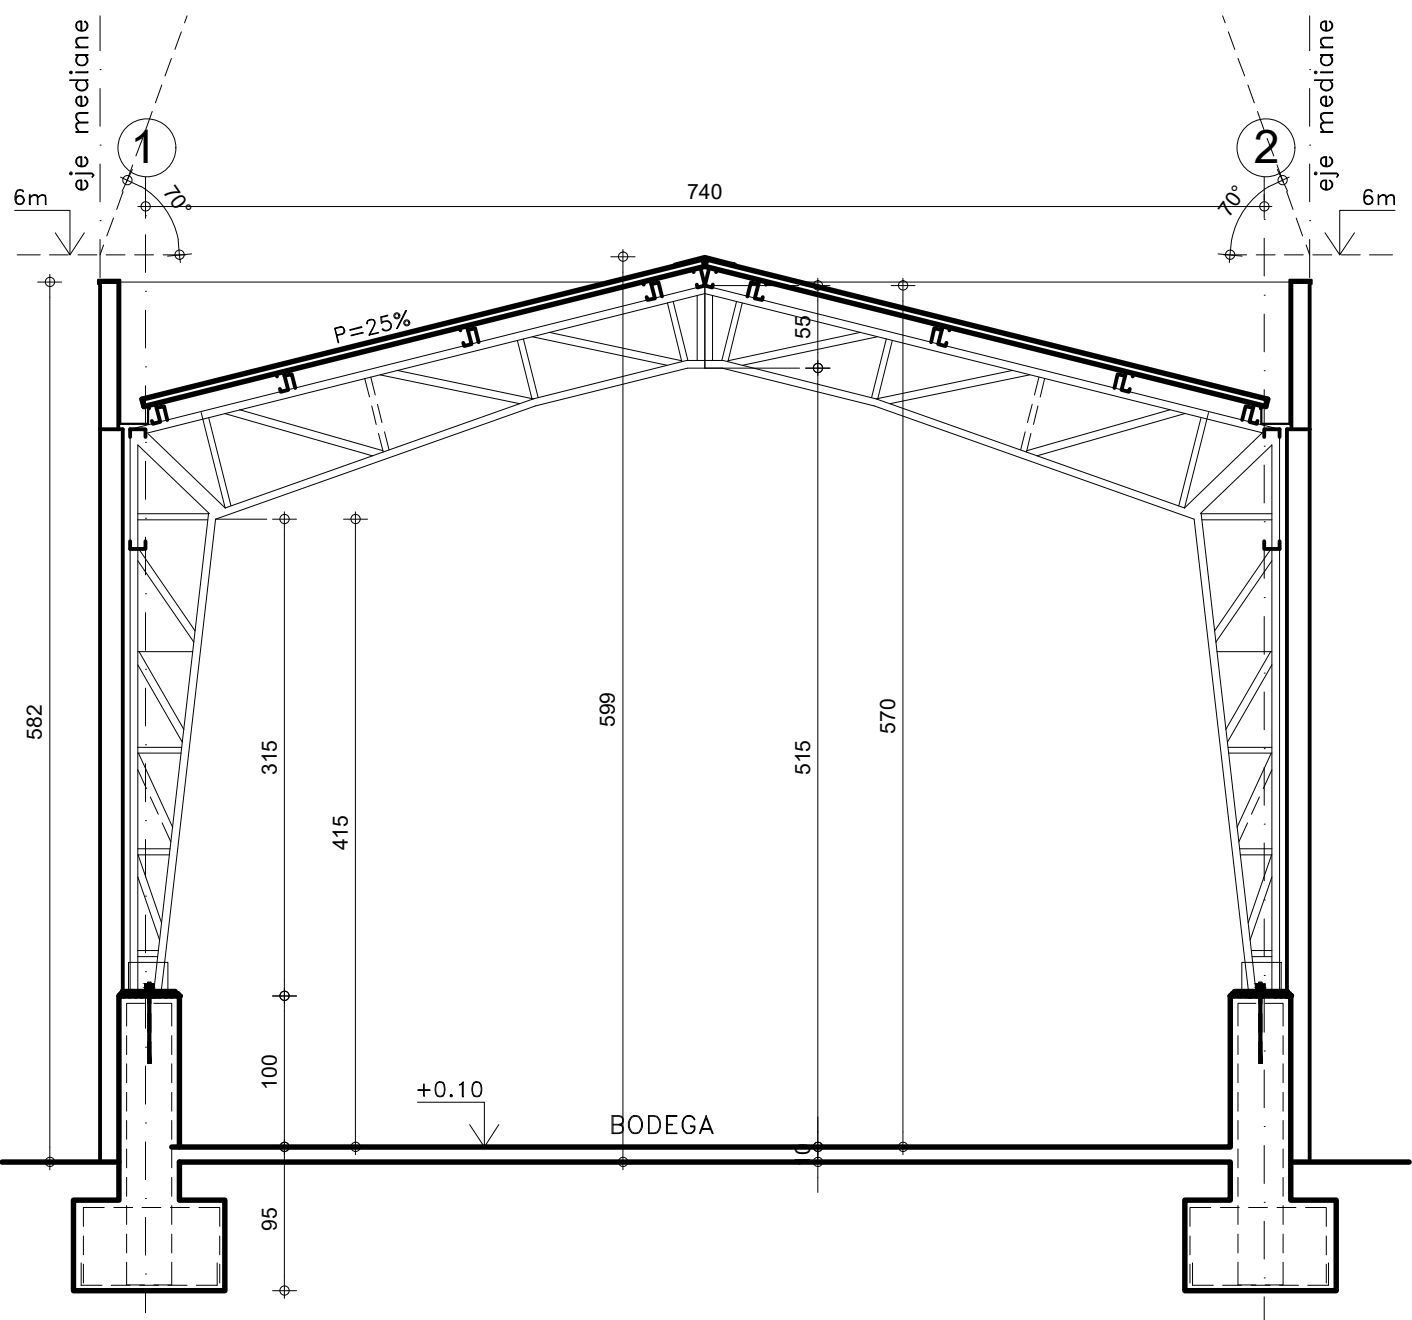



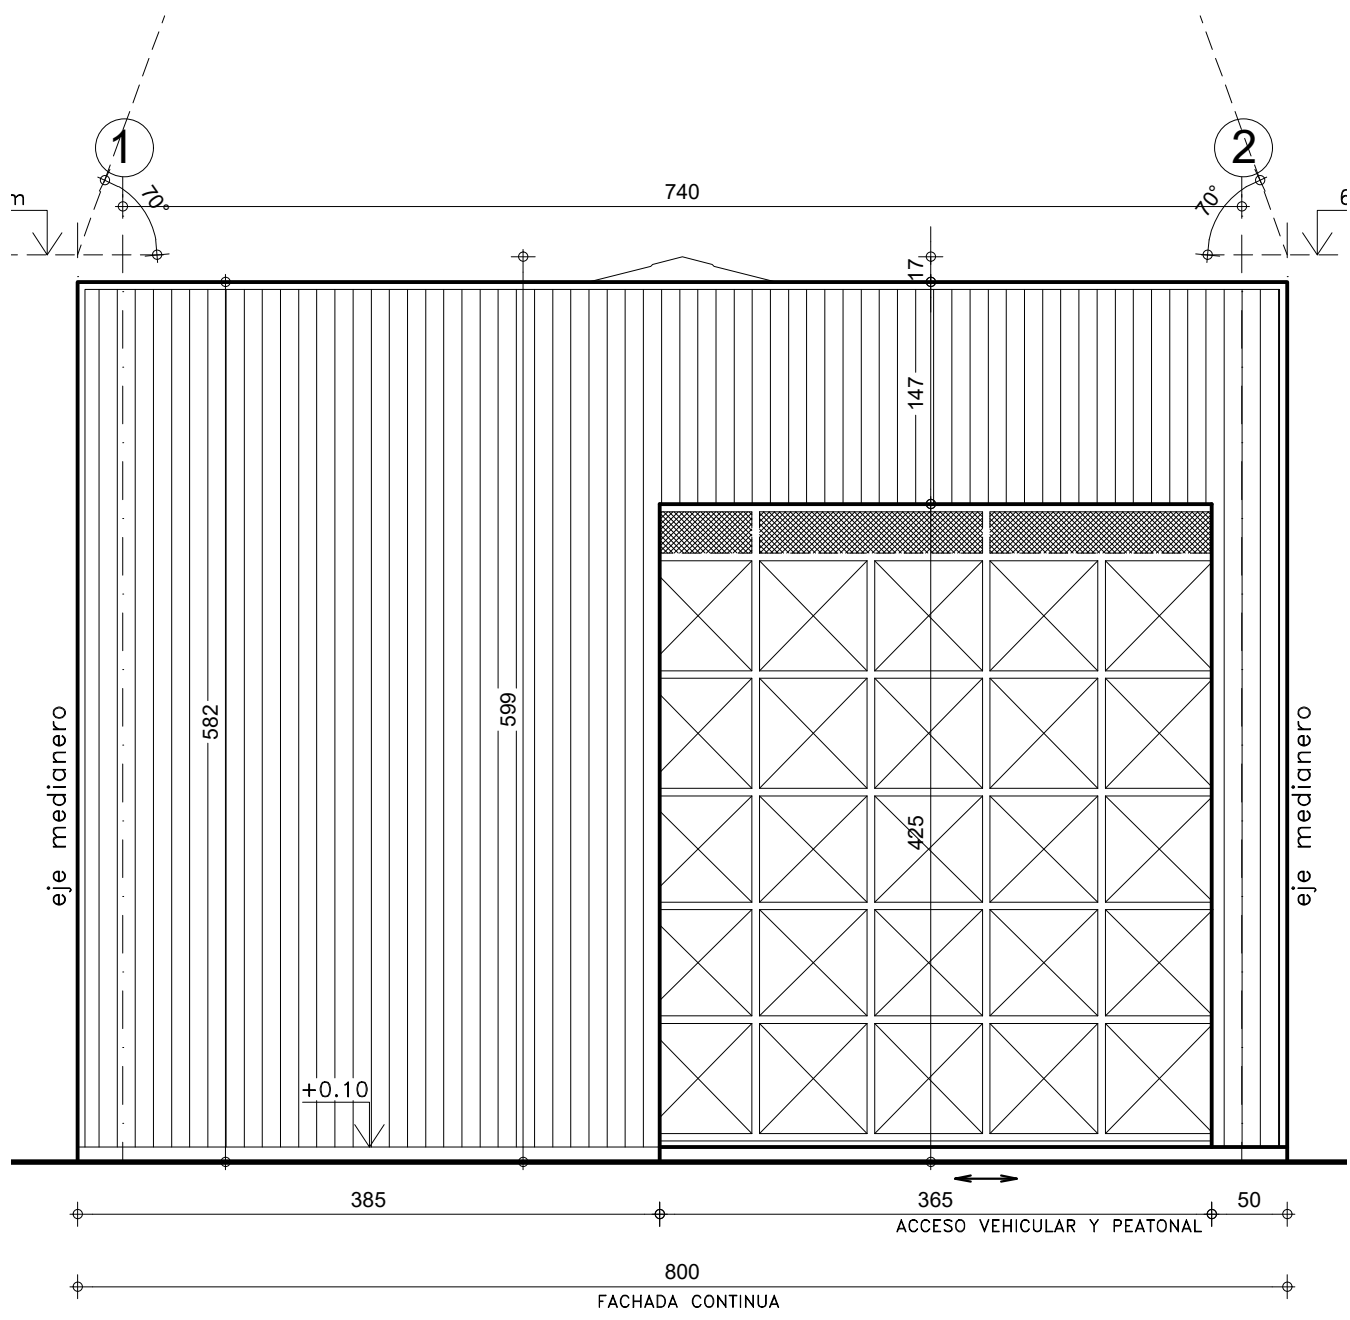


1 ELEVACION ORIENTE (CALLE URUGUAY)  
1:50


2 CORTE A-A  
1:50

3 CORTE B-B  
1:50

4 CIERRO CALLE  
1:50

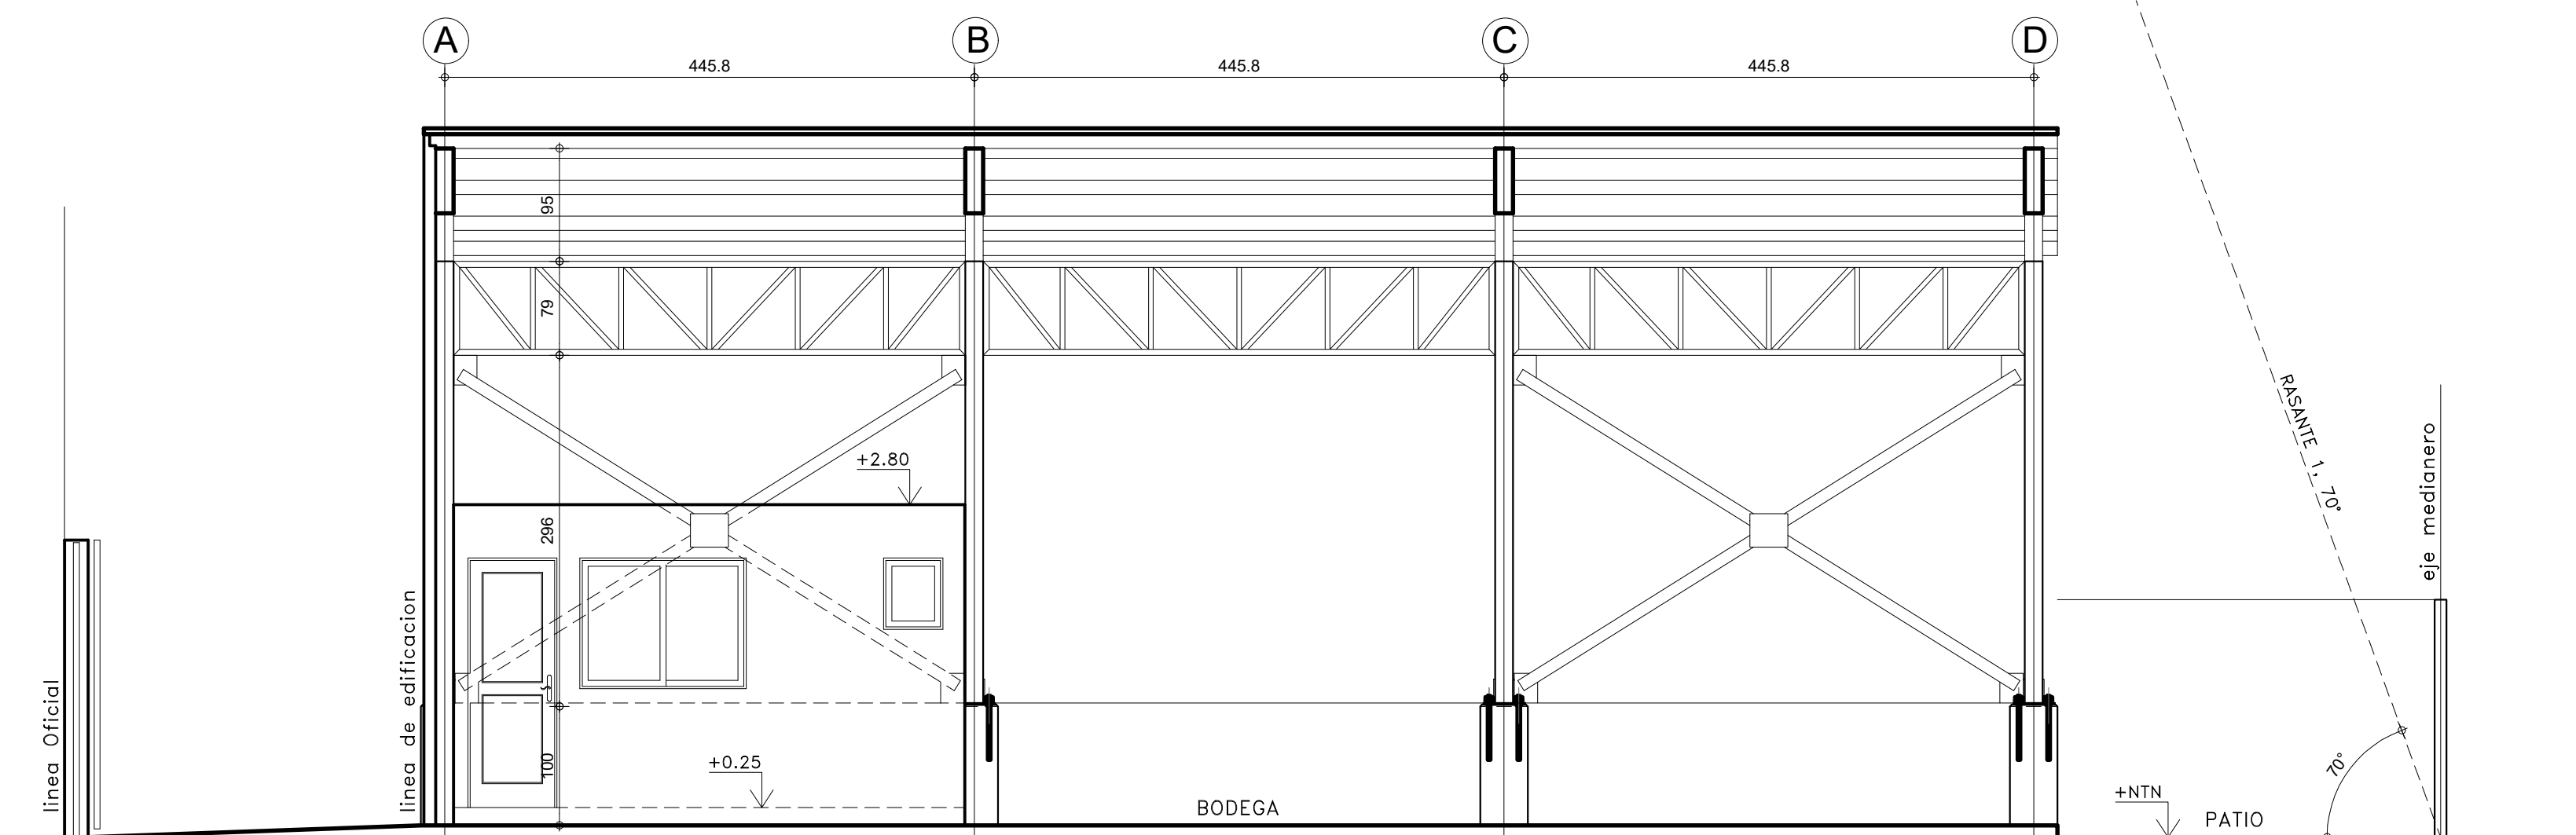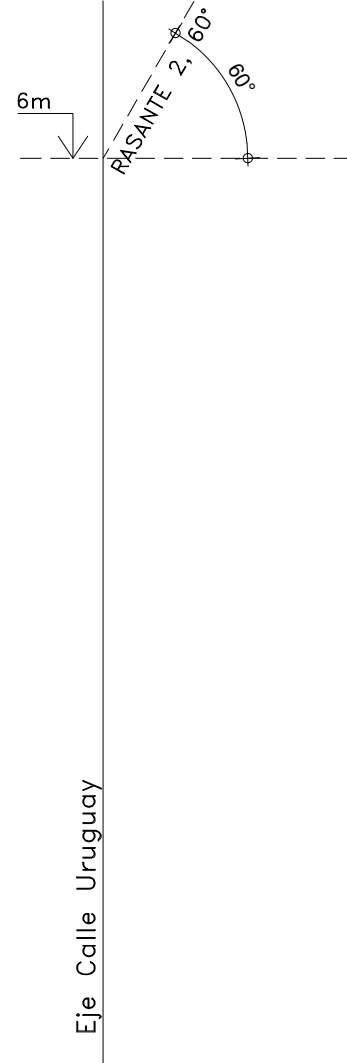

5 CORTE ELEVACION C-C  
1:50

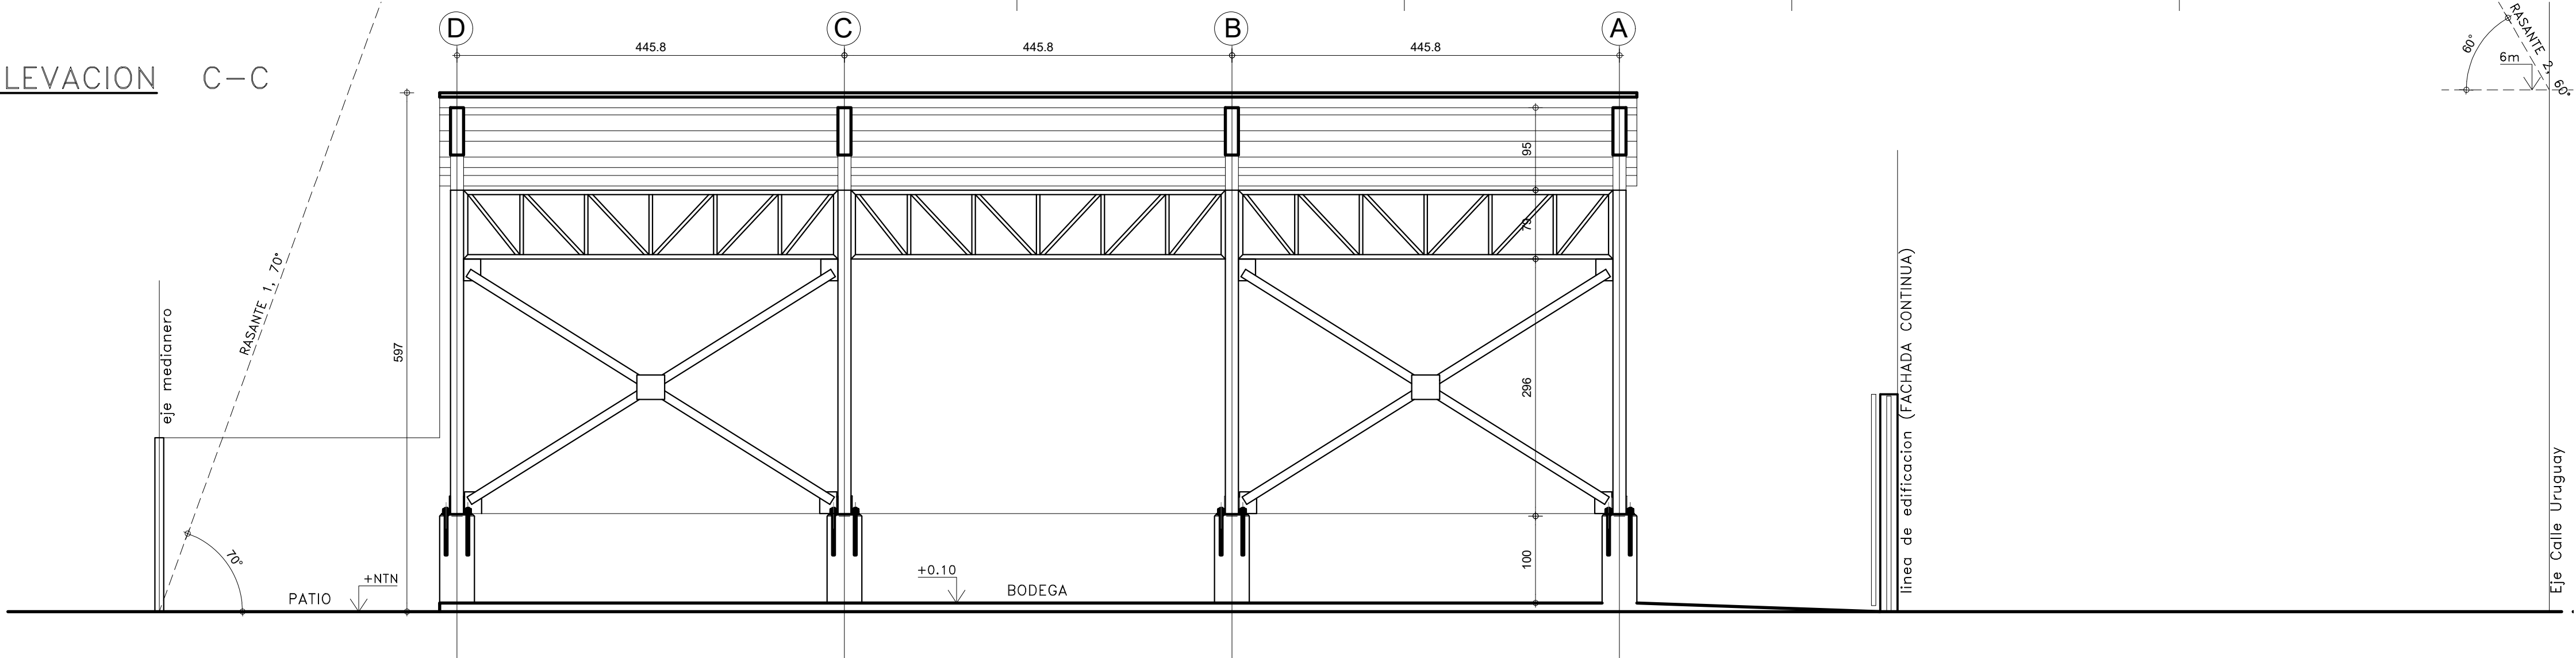

6 CORTE- ELEVACION D-D  
1:50

|                                            |  |  |  |                                                                |  |
|--------------------------------------------|--|--|--|----------------------------------------------------------------|--|
| OBRA NUEVA<br>BODEGA COMPLEMENTARIA TIPO 2 |  |  |  | UBICACION : URUGUAY Nº3134                                     |  |
| ILUSTRE MUNICIPALIDAD DE RECOLETA          |  |  |  | COMUNA : RECOLETA                                              |  |
| MATERIA<br>ELEVACIONES<br>CORTES           |  |  |  | PROPIETARIO<br>PABLO ERNESTO RIVERA ONETTO<br>C.I. 8.926.691-9 |  |
| DIBUJO<br>JOSE SAEZ I.                     |  |  |  | ARQUITECTO<br>GUSTAVO RIOSERO MARTINEZ<br>C.I. 10.390.900-7    |  |
| REVISOR<br>G.R.M.                          |  |  |  | ROL<br>6070-15                                                 |  |
| ESCALA<br>INDICADAS                        |  |  |  | FECHA<br>11-06-20                                              |  |